



Схема электрическая
соединений станка

Станция охлаждения

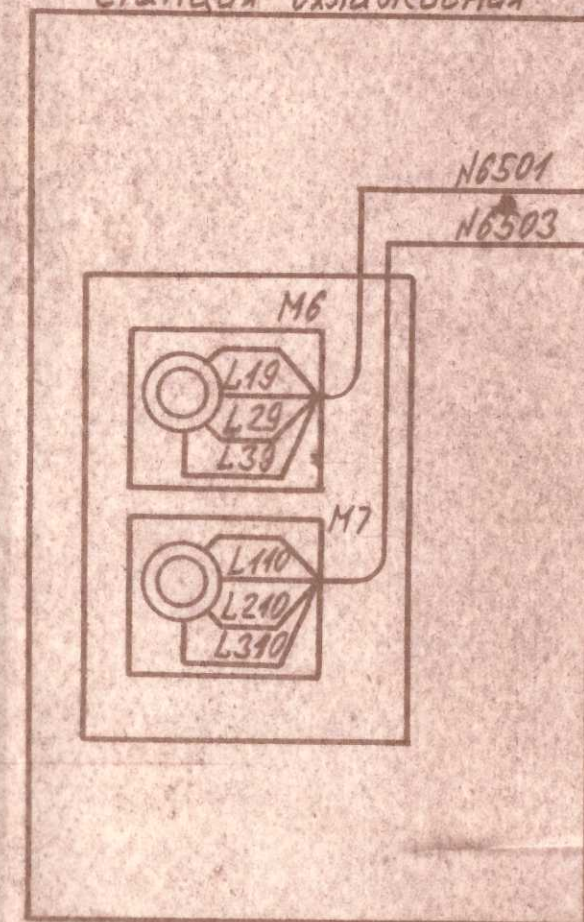

Блок реверса суппорта
ОШ-450.80.4.040.0.0034
Схема электрическая
соединений

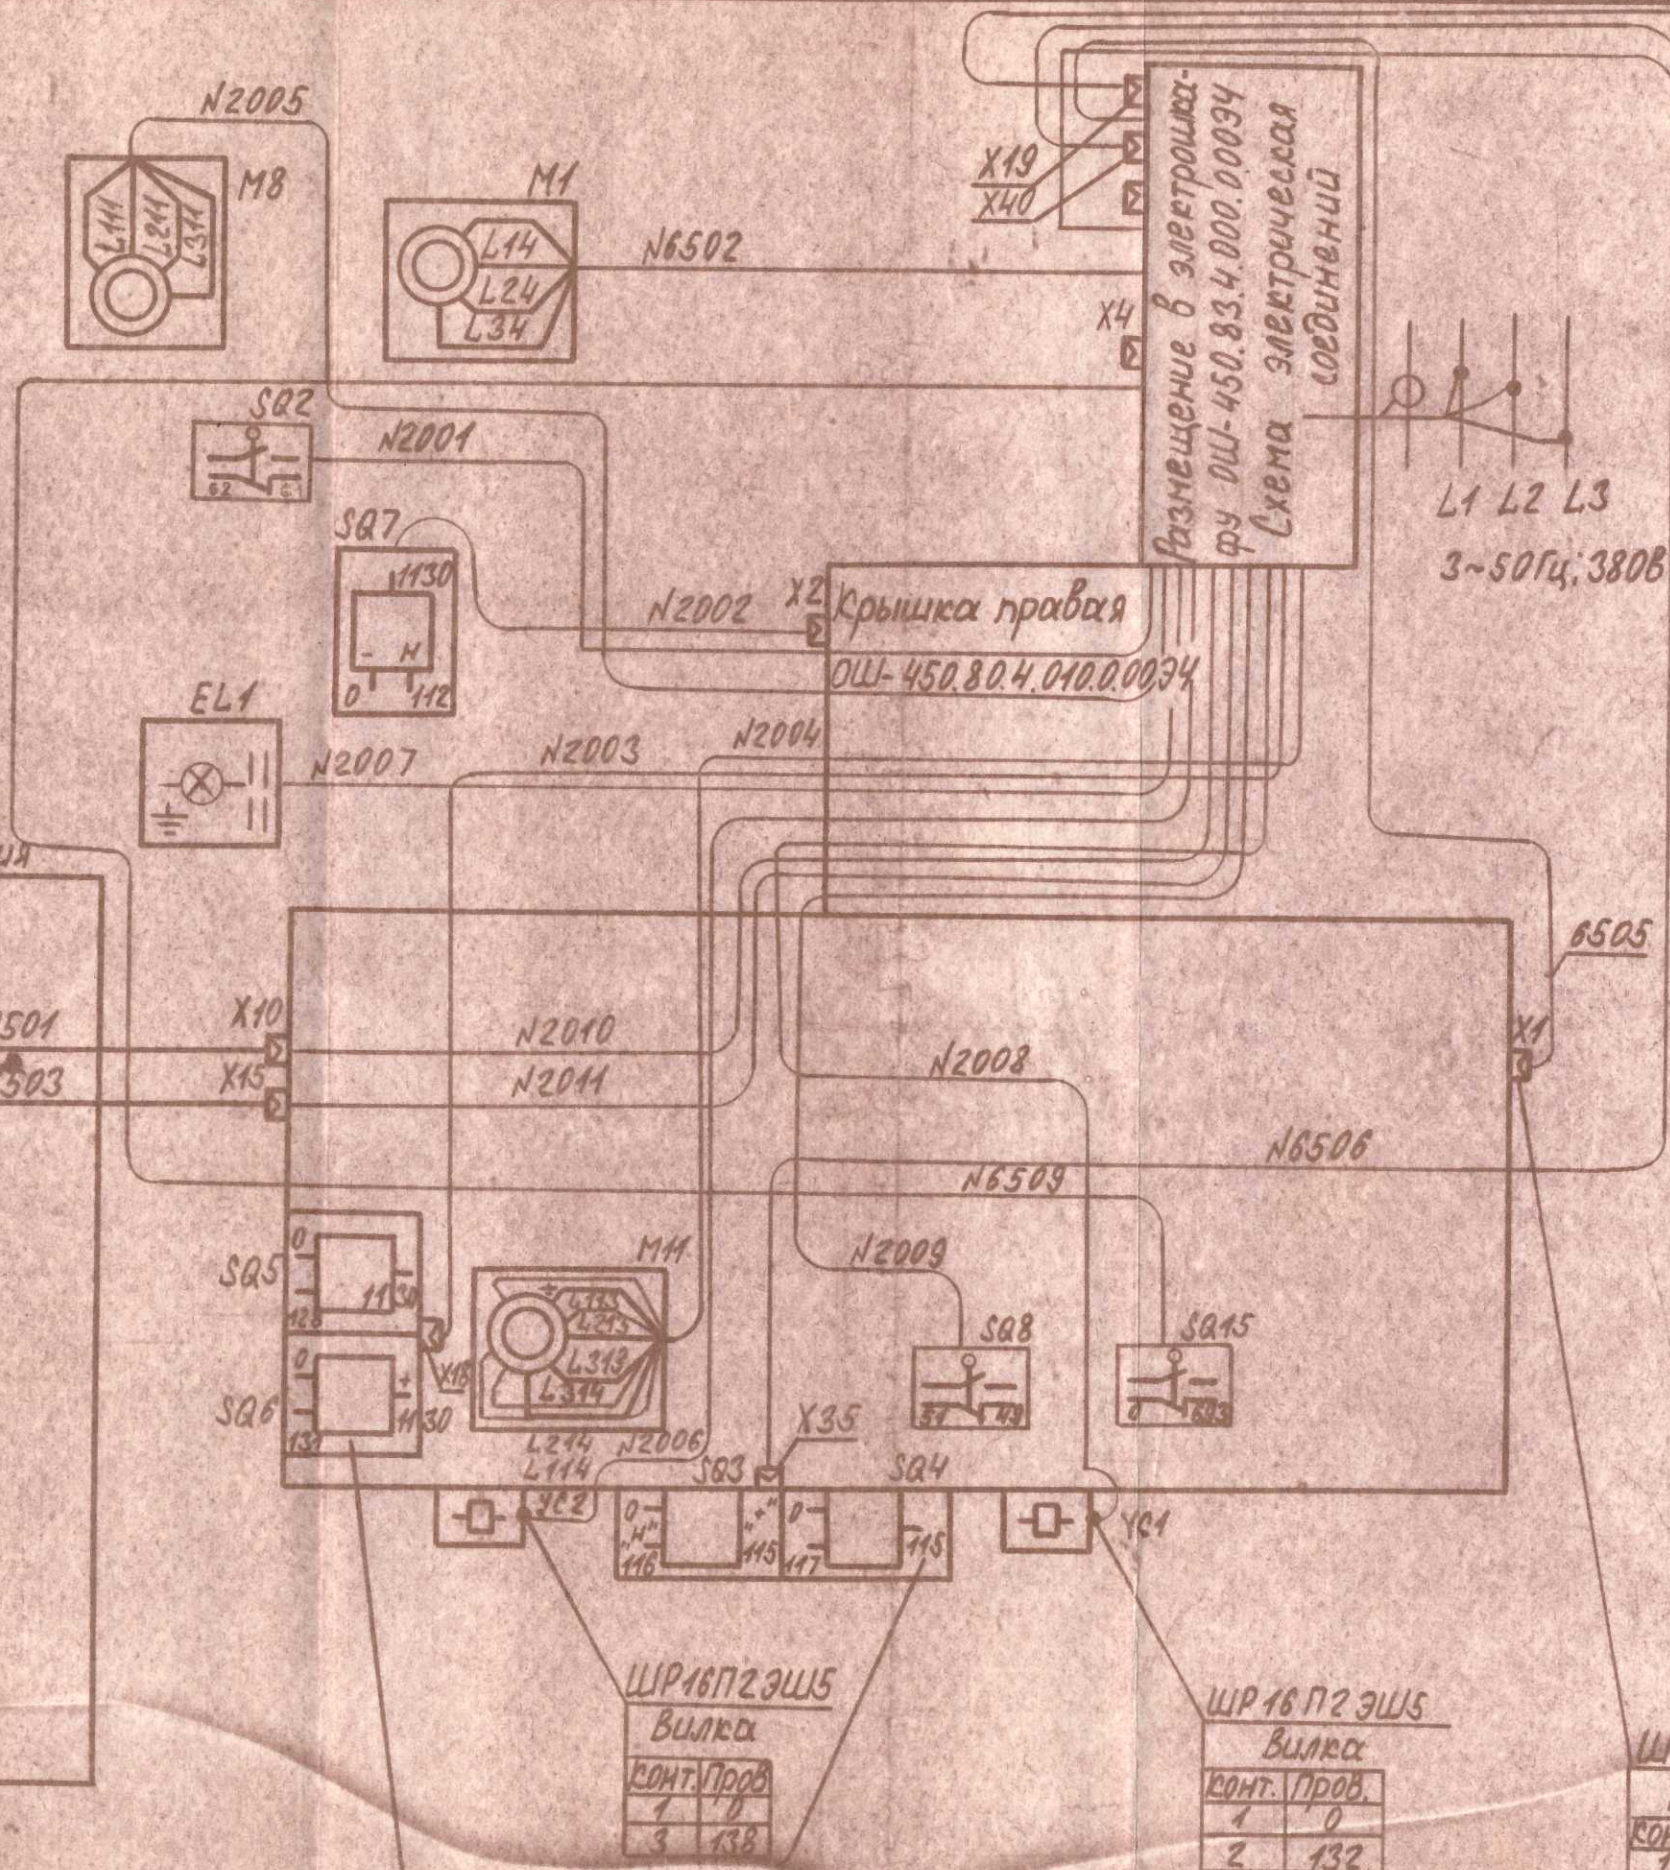

ШР16П2ЭШ5
Вилка

Конт.	Пров.
1	0
3	138


ШР16П2ЭШ5
Вилка

Конт.	Пров.
1	0
2	132

ШР20П5НШ10
Вилка

Конт.	Пров.
1	123
2	123
3	126
4	132
5	+

Гидростанция

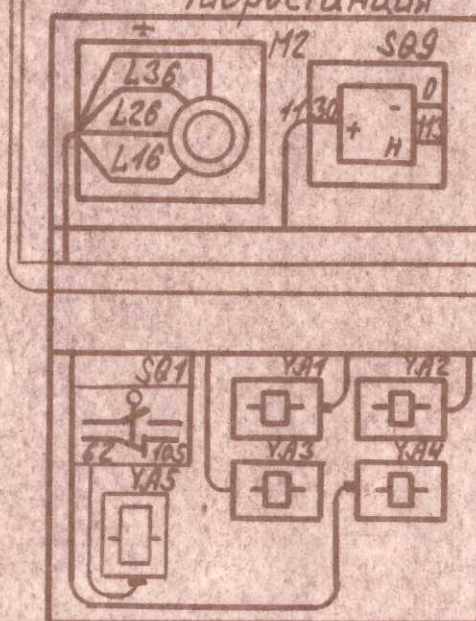

Пульт
управления
ОШ-450.84.8
000.0.0034

Блок реверса стола
ОШ-450.80.4.025.0.0034
Схема электрическая
соединений